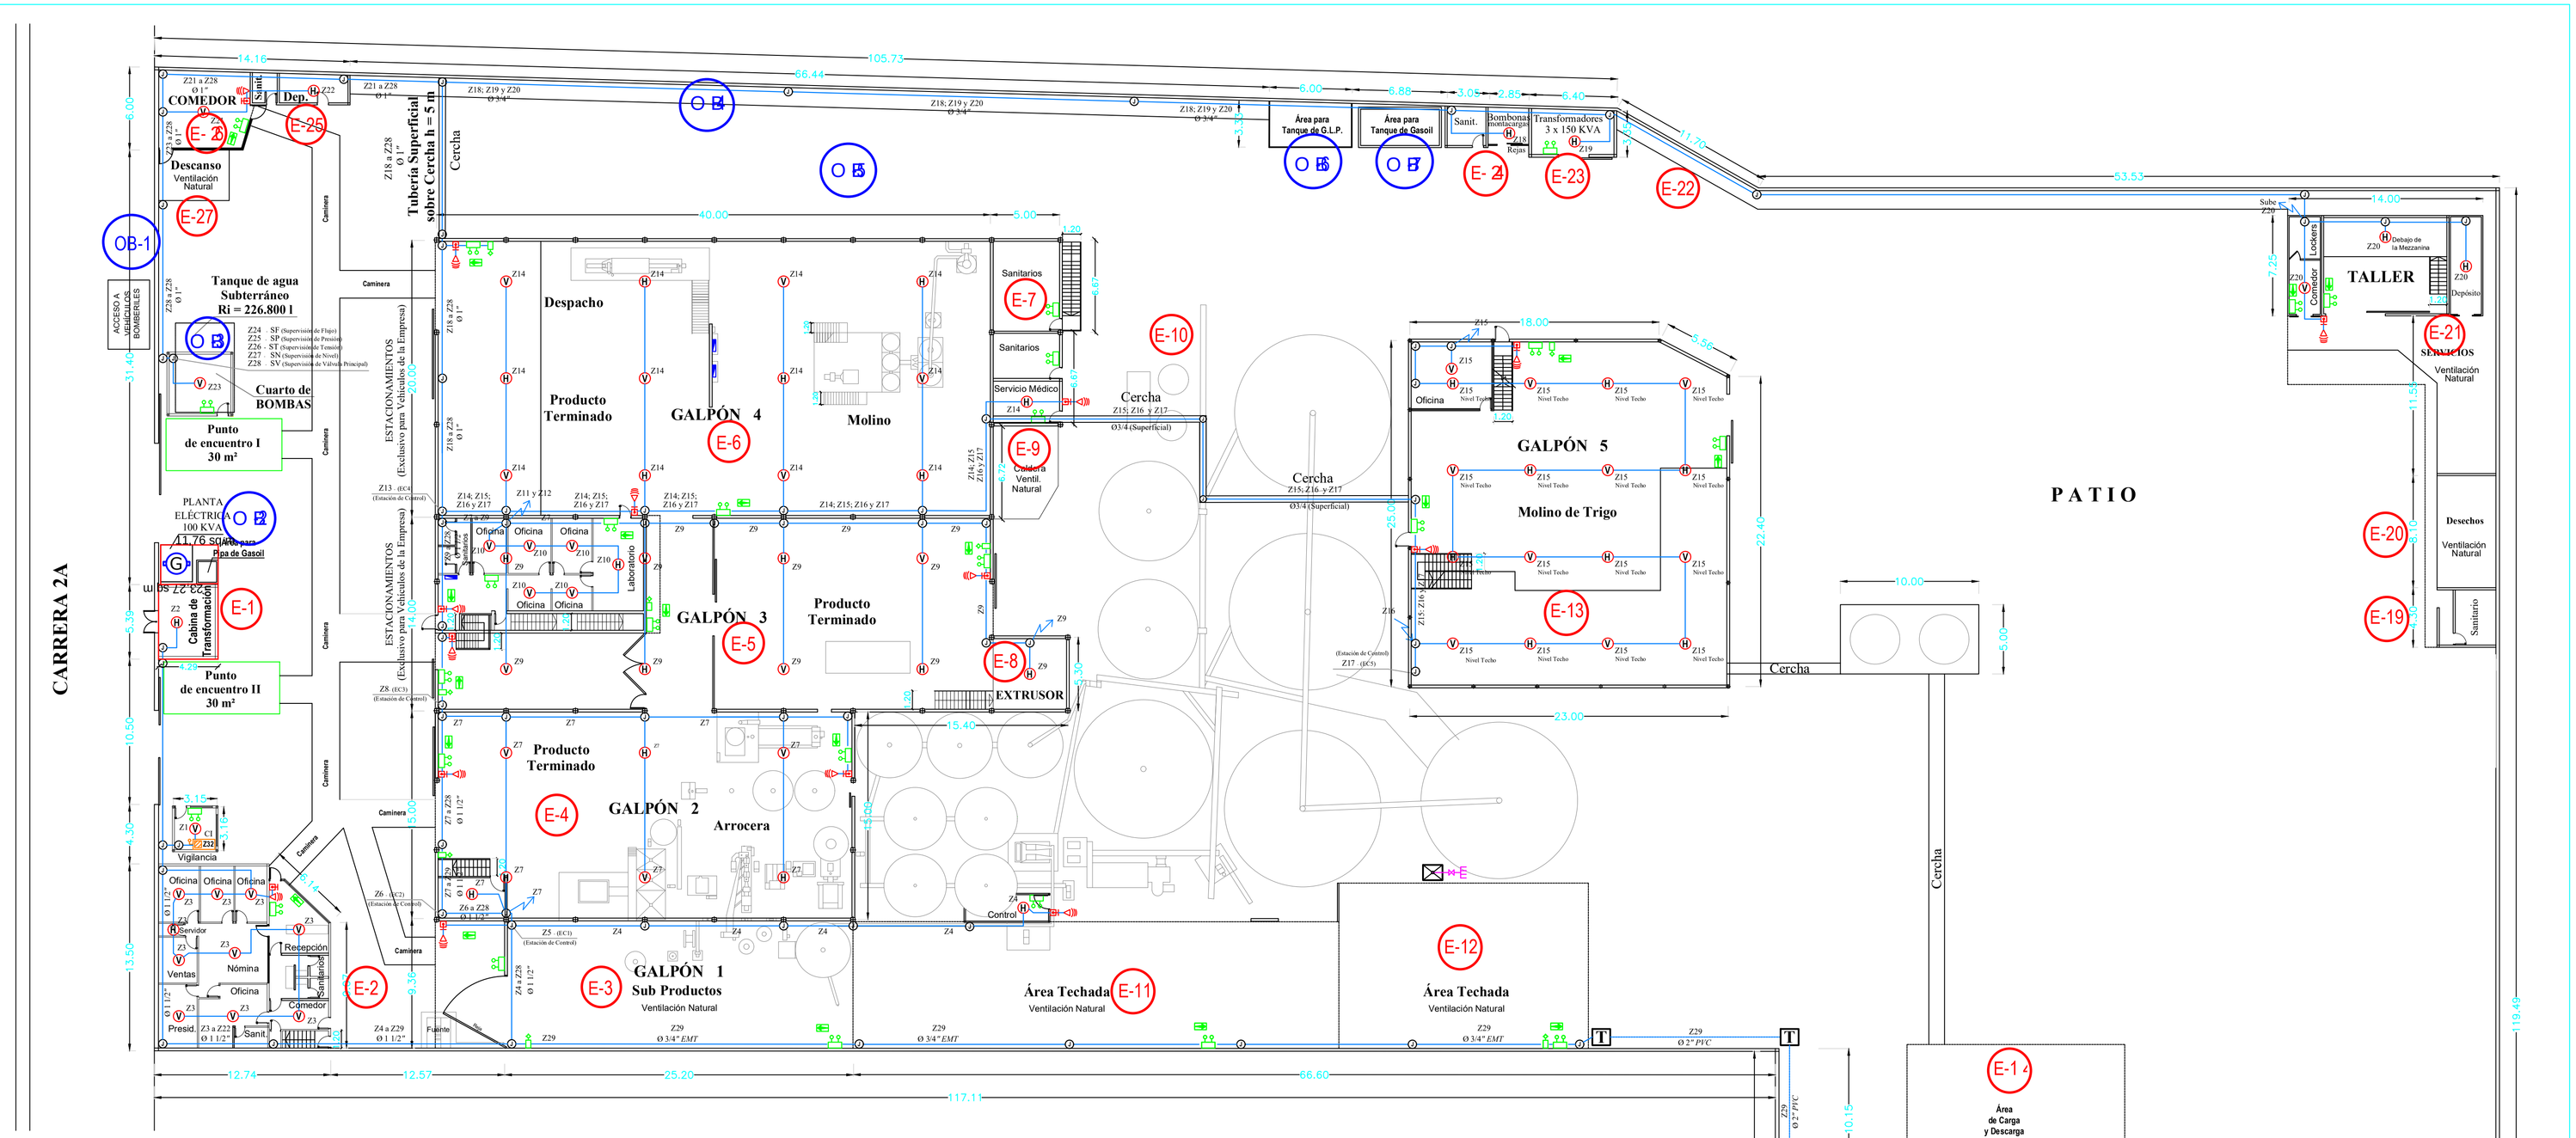

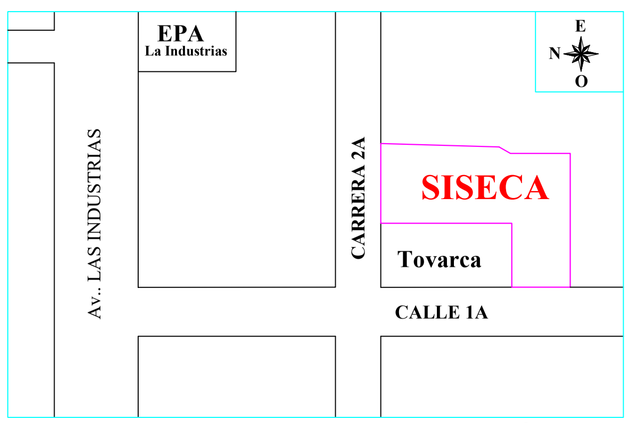

SITUACIÓN S/Escala

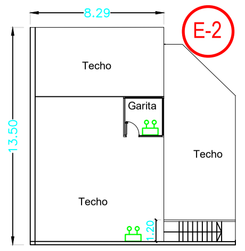

2do Nivel (Oficinas)

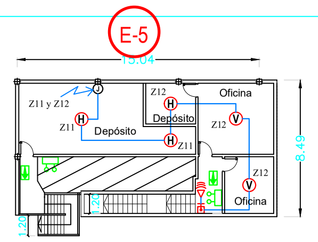

2do Nivel (Oficinas Galpón 3)

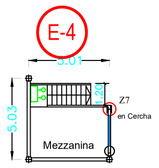

MEZZANINA (Control de Inventario Galpón 2)

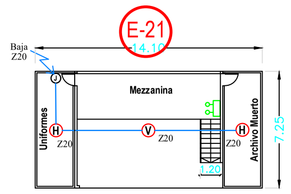

2do Nivel (Taller)

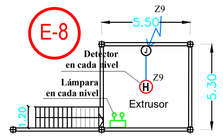

Extrusor (4 Niveles Galpón 3)

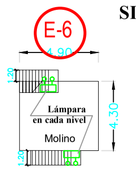

2do Nivel Molino (4 Niveles Galpón 4)

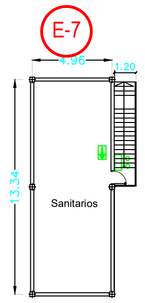

2do Nivel (Galpón 4)

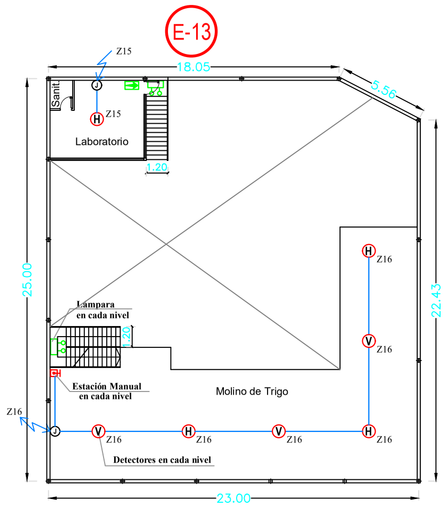

Molino de Trigo Galpón 5 (4 Niveles)

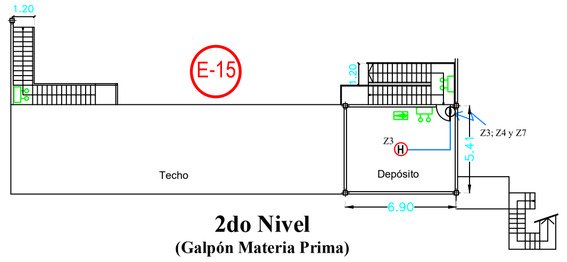

2do Nivel (Galpón Materia Prima)

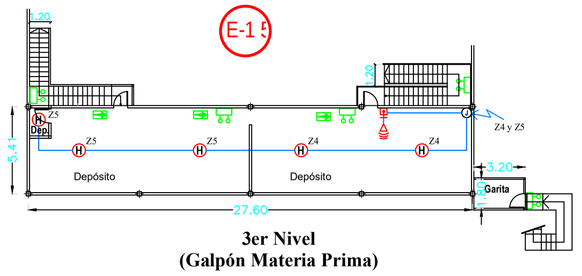

3er Nivel (Galpón Materia Prima)

NOTAS:

1.- Para el Sistema de Alarma y Detección de Incendios, salvo otra indicación el Conductor será del Tipo TF # 16 AWG y la Tubería Superficial será del Tipo EMT de Ø 3/4". * (Ver Nota 3)

2.- La tubería Subterránea entre Tanquillas será del Tipo PVC de Ø 2".

3.- Las Instalaciones para el Sistema de Alarma y Detección Contra Incendios e Iluminación de Emergencia, así como los equipos a instalar, en las zonas de Clasificación II, serán "A PRUEBA DE IGNICIÓN DE POLVO".

L E Y E N D A

- Tablero Eléctrico
- Z32 — Central de Incendios de 32 Zonas con Comunicación Verbal (CM 16 / 32 200 W - 2)
- Z8 — Central de Incendios de 8 Zonas
- V — Detector de Calor de Velocidad de Incremento de Temperatura
- H — Detector de Óptico de Humo (Fotoeléctrico)
- Difusor de Sonido
- Estación Manual de Alarma Compuesta
- J — Caja de Paso o Empalme
- Lámpara de Emergencia de 2 Faros
- Señalización de Medios de Escape
- Lámpara Portátil
- T — Tanquilla
- Pararrayos
- Tubería Superficial
- Tubería Subterránea

SISECA

Silos y Secado C. A.

J08517287-4

Carrera 2A con Calle 1A - Local S/N
Zona Industrial III
Parroquia Guerrera Ana Soto
Municipio Iribarren
Barquisimeto - Estado Lara

PROYECTO:

DECRETO 2.195
(Reglamento sobre Prevención de Incendios)

TIPO DE OCUPACIÓN:

INDUSTRIAL de Gran Riesgo
ALMACÉN (Depósito Riesgo Moderado, A < 1500 m²)
OFICINAS (Fachada Convencional h ≤ 25 m)
LABORATORIO (Industrial N = 1; A ≤ 25 m²)
SITIO DE REUNIÓN (Comedor)
TALLER (Mantenimiento)
ESTACIONAMIENTO (Vehículos Automotores de un Nivel a cielo abierto)

CONTENIDO:

SISTEMA DE DETECCIÓN, ALARMA, LÁMPARAS DE EMERGENCIA AUTOCONTENIDAS, SEÑALIZACIÓN DE MEDIOS DE ESCAPE, PUNTOS DE ENCUENTRO - CAMINERÍAS

PROPIETARIO:	INGENIERO:
MARÍA G. HERNÁNDEZ DE BARBIERI	C.I.V.: 19.870 ING. RAFAEL C. SÁNCHEZ TLF: 0414 5291684

ESCALA:	FECHA:	HOJA:	SERIE:
Tamaño: Pliego 1:250	12 / 2021	1 DE 2	SCI-01