

Sete (7)



Alcaldía Municipal de  
**Iribarren**

RIF G20114703

República Bolivariana de Venezuela  
Estado Lara  
Alcaldía del Municipio Iribarren  
Servicio Municipal de Administración Tributaria

# **CERTIFICADO DE SOLVENCIA**



**SEMAT**  
Servicio Municipal de Administración Tributaria  
El Orden en los Pagos

N°SMIU022159

|                            |                                                                  |                                 |                    |
|----------------------------|------------------------------------------------------------------|---------------------------------|--------------------|
| TIPO DE SOLVENCIA:         |                                                                  | FECHA EXPEDICIÓN:               | FECHA VENCIMIENTO: |
| INMUEBLES URBANOS          |                                                                  | 30-05-2018                      | 31-12-2018 ✓       |
| N° DE LICENCIA/CÓDIGO SAP: | N° RIF. O CÉDULA:                                                | NOMBRE DEL CONTRIBUYENTE:       |                    |
| 40170975                   | J-085172874                                                      | SILOS Y SECADO, C.A ( SISECA) ✓ |                    |
| CÓDIGO CATASTRAL:          | DIRECCIÓN DEL CONTRIBUYENTE:                                     |                                 |                    |
| 017000901000               | ZONA IND III, CRR 2-A E/ CLL.1A Y QUEBRADA LA RUEZGA N°. S/N°. ✓ |                                 |                    |

## **DESCRIPCIÓN:**

QUIEN SUSCRIBE, GERENTA GENERAL(E) DEL SERVICIO MUNICIPAL DE ADMINISTRACIÓN TRIBUTARIA DE LA ALCALDÍA DEL MUNICIPIO IRIBARREN, DANDO CUMPLIMIENTO A LO ESTABLECIDO EN EL ART. 95 DE LA ORDENANZA DE HACIENDA PÚBLICA MUNICIPAL, PREVIA VERIFICACIÓN POR EL SISTEMA, CERTIFICA LA RECEPCIÓN DE LOS PAGOS CORRESPONDIENTES AL IMPUESTO SOBRE INMUEBLE URBANO, QUE IGUALMENTE SE CONSTATÓ EL PAGO DE LA TASA SEGÚN RECIBO NRO: PTU500029905 , DE FECHA: 21-05-2018, EXPEDIDA POR LA GERENCIA DE RECAUDACIÓN.

LA PRESENTE CERTIFICACIÓN NO EXCLUYE LAS FACULTADES DEL FISCO MUNICIPAL PARA REALIZAR LAS REVISIONES PERTINENTES DE CONFORMIDAD CON EL ORDENAMIENTO JURÍDICO APLICABLE.

EN BARGUISIMETO A LOS TREINTA(30) DIAS DEL MES DE MAYO DEL AÑO DOS MIL DIECIOCHO(2018).

La validez de este comprobante puede verificarse a través de los teléfonos: (0251)-2333285/2331448

ELABORADO POR:

*Enna Tovar*

NOMBRE FUNCIONARIO: ENNA TOVAR

CARGO FUNCIONARIO: ESP. EN INFORMATICA I

*[Firma]*

GERENTA GENERAL (E) DEL SEMAT

SELLO



\* 87A5743CAF6515CC418D6BDBAB6AE0A1 \*





República Bolivariana de Venezuela  
Alcaldía del Municipio Iribarren  
Barquisimeto, Estado Lara  
Dirección de Catastro



Alcaldía del Municipio de  
**Iribarren**

Fecha: 28-02-2018  
Solicitud Nro: 192-2017

## CÉDULA CATASTRAL

Código Verificación: 5a96f1159fe66

| PROPIETARIOS DEL INMUEBLE                               |   | CÉDULA / RIF           |               | CÓDIGO CATASTRAL     |                                                    |
|---------------------------------------------------------|---|------------------------|---------------|----------------------|----------------------------------------------------|
| SILOS Y SECADO, C.A. (SISECA)                           |   | J085172874             |               | ANTERIOR             | 13-03-05-U01-223-0002-015-000                      |
|                                                         |   |                        |               | ACTUAL               | 13-03-04-U01-017-0009-013-000                      |
| DIRECCIÓN: CARRERA 2A ENTRE CALLE 1A QUEBRADA LA RUEZGA |   |                        |               |                      |                                                    |
| SECTOR / ZONA                                           | ZONA INDUSTRIAL III   | NÚMERO                 | S/Nº          | PARROQUIA            | Juan de Villegas                                   |
| BALANCE DE SUPERFICIE                                   |   |                        |               |                      |                                                    |
| Área Original                                           |   | Área Actual            |               | Diferencia           |                                                    |
| 9.157,30 (m²)                                           |   | 12.568,88 (m²)         |               | 3.411,58 (m²)        |                                                    |
| DATOS DE LOS DOCUMENTOS DE PROPIEDAD                    |   |                        |               |                      |                                                    |
| Número                                                  | Asto.Reg./ Tomo   | Matricula / Prot.      | Folio         | Fecha                | Entidad Pública Legal                              |
| 2017.667                                                | 1   | 363.11.2.7.5268        | Real Año 2017 | 20-10-2017           | Registro Público del Segundo Circuito de Iribarren |
| LINDEROS ORIGINALES S/Nº                                |   |                        |               |                      |                                                    |
| NORTE                                                   | En dos líneas de: (61,68 Mts) y (69,91 Mts) con Carrera 2-A.                                                                          |                        |               |                      |                                                    |
| SUR                                                     | En dos líneas de: (6,01 ;ts) y (120,75 Mts), con terreno desocupado.                                                                  |                        |               |                      |                                                    |
| ESTE                                                    | En tres líneas de: (104,63 Mts), con Proyecto de canalización del parque la Ruezga y (2,22 Mts), (53,64 Mts), con Quebrada la Ruezga. |                        |               |                      |                                                    |
| OESTE                                                   | En dos líneas de: (153,35 Mts) y (16,71 Mts), con la Calle 1A.                                                                        |                        |               |                      |                                                    |
| LINDEROS ACTUALES                                       |   |                        |               |                      |                                                    |
| NORTE                                                   | Con parcela que es o fue de Silos y Secados, C.A. y Carrera 2A de la referida Zona Industrial, que es su frente.                      |                        |               |                      |                                                    |
| SUR                                                     | Con Quebrada la Ruezga.   |                        |               |                      |                                                    |
| ESTE                                                    | Con Quebrada la Ruezga.   |                        |               |                      |                                                    |
| OESTE                                                   | Con parcela que es o fue de Silos y Secados, C.A.; Corporación Rigz, C.A. y Tovar, C.A.                                               |                        |               |                      |                                                    |
| VALOR TERRENO                                           |   | VALOR CONSTRUCCIÓN     |               | TOTAL VALOR INMUEBLE |                                                    |
| 4.293.857,97 Bs                                         |   | 55.339.876,80 Bs       |               | 59.633.734,77 Bs     |                                                    |
|                                                         |   |                        |               | Nº MAPA CATASTRAL    |                                                    |
|                                                         |   |                        |               | 6346-III-SO          |                                                    |
| INFORMACIÓN SOLO PARA FINES FISCALES                    |   |                        |               |                      |                                                    |
| RÉGIMEN DE PROPIEDAD                                    |   | ÁREA ORIGINAL TERRENO  |               | TOTAL ÁREA ORIGINAL  |                                                    |
| Privado individual                                      |   | 9.157,30 (m²)          |               | 9.157,30 (m²)        |                                                    |
|                                                         |   |                        |               | ÁREA ACTUAL          |                                                    |
|                                                         |   |                        |               | 12.568,88 (m²)       |                                                    |
| BASE IMPONIBLE PARA DETERMINAR IMPUESTO INMOBILIARIO    |   |                        |               |                      |                                                    |
| ÁREA FISCAL DE TERRENO                                  |   | TIPOLOGÍA CONSTRUCCIÓN |               | USO                  |                                                    |
| 9.157,30 (m²)                                           |   | Galpon Industrial      |               | Industrial           |                                                    |
|                                                         |   |                        |               | ÁREA CONSTRUCCIÓN    |                                                    |
|                                                         |   |                        |               | 4.112,96 (m²)        |                                                    |



OBSERVACIONES:

- 1) Se dejan a salvo derechos de terceros y del Municipio sobre la propiedad del terreno.
- 2) Sujeta a las afectaciones que esta pudiese tener en cumplimiento de la función social que ejecuta el Municipio, en materia de urbanismo.
- 3) Existe una diferencia en más de 3.411,58 m<sup>2</sup> entre el Área según documento protocolizado y Área del plano de mensura, ya que dicho documento presenta un error en cuanto a medidas (linderos), siendo lo correcto la cabida que el Municipio vende. Se le exhorta realizar corrección de la misma.
- 4) Igualmente dicho excedente (Ejido) presenta una Zonificación por: Zona de Protección Urbana (Z.P.U.), Línea Ferrea y Parque Recreacional La Rueda según Decreto N° 1.650 de fecha 05 de Junio del Año 1991 Gaceta Oficial 4409 Extraordinaria del 04 de Abril del Año 1992, según Zonificación emitida por el Área Física adscrita a esta Dirección en fecha 26/02/2018.
- 5) Área según documento: 9.157,30 m<sup>2</sup> por la cual se otorga la presente Cédula Catastral; Área según Plano de Mensura: 12.568,88 m<sup>2</sup>. Área ocupada fuera del documento (Ejido): 3.411,58 m<sup>2</sup>.
- 6) A solicitud de parte interesa las parcelas 017-0009-003-000 (Ant.223-0002-009-000); 017-0009-004-000 (Ant.223-0002-010-000) y 017-0009-009-000 (Ant.223-0002-002-000) se integran dando origen a la Pc. 017-0009-013-000 (Ant. 223-0002-015-000).
- 7) Esta solicitud de integración, fue realizada con antelación a la emisión del Reglamento de Integración y División de Parcelas.
- 8) El Artículo N° 67 de la Ley Orgánica de Ordenación Urbanística establece: "Las parcelas integradas, serán consideradas como una unidad a los efectos Urbanísticos y en ningún caso, podrán subdividirse nuevamente a los fines de su utilización.




Ing. Christian E. Mendoza C  
Director de Catastro

Resolución N° RRHHAL 211-2017 del 20-09-2017

DIRECCIÓN DE

| Retirado por | Cédula de Identificación | Fecha    | Firma   | Revisado por |
|--------------|--------------------------|----------|---------|--------------|
| JOSÉ VIDA    | 7.306.893                | 11/05/18 | [Firma] | [Firma]      |

Elaborado por: Francis D. Colmenarez B.

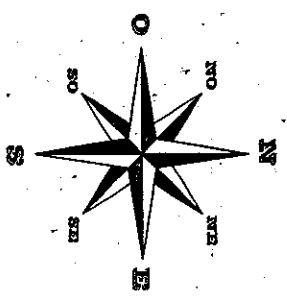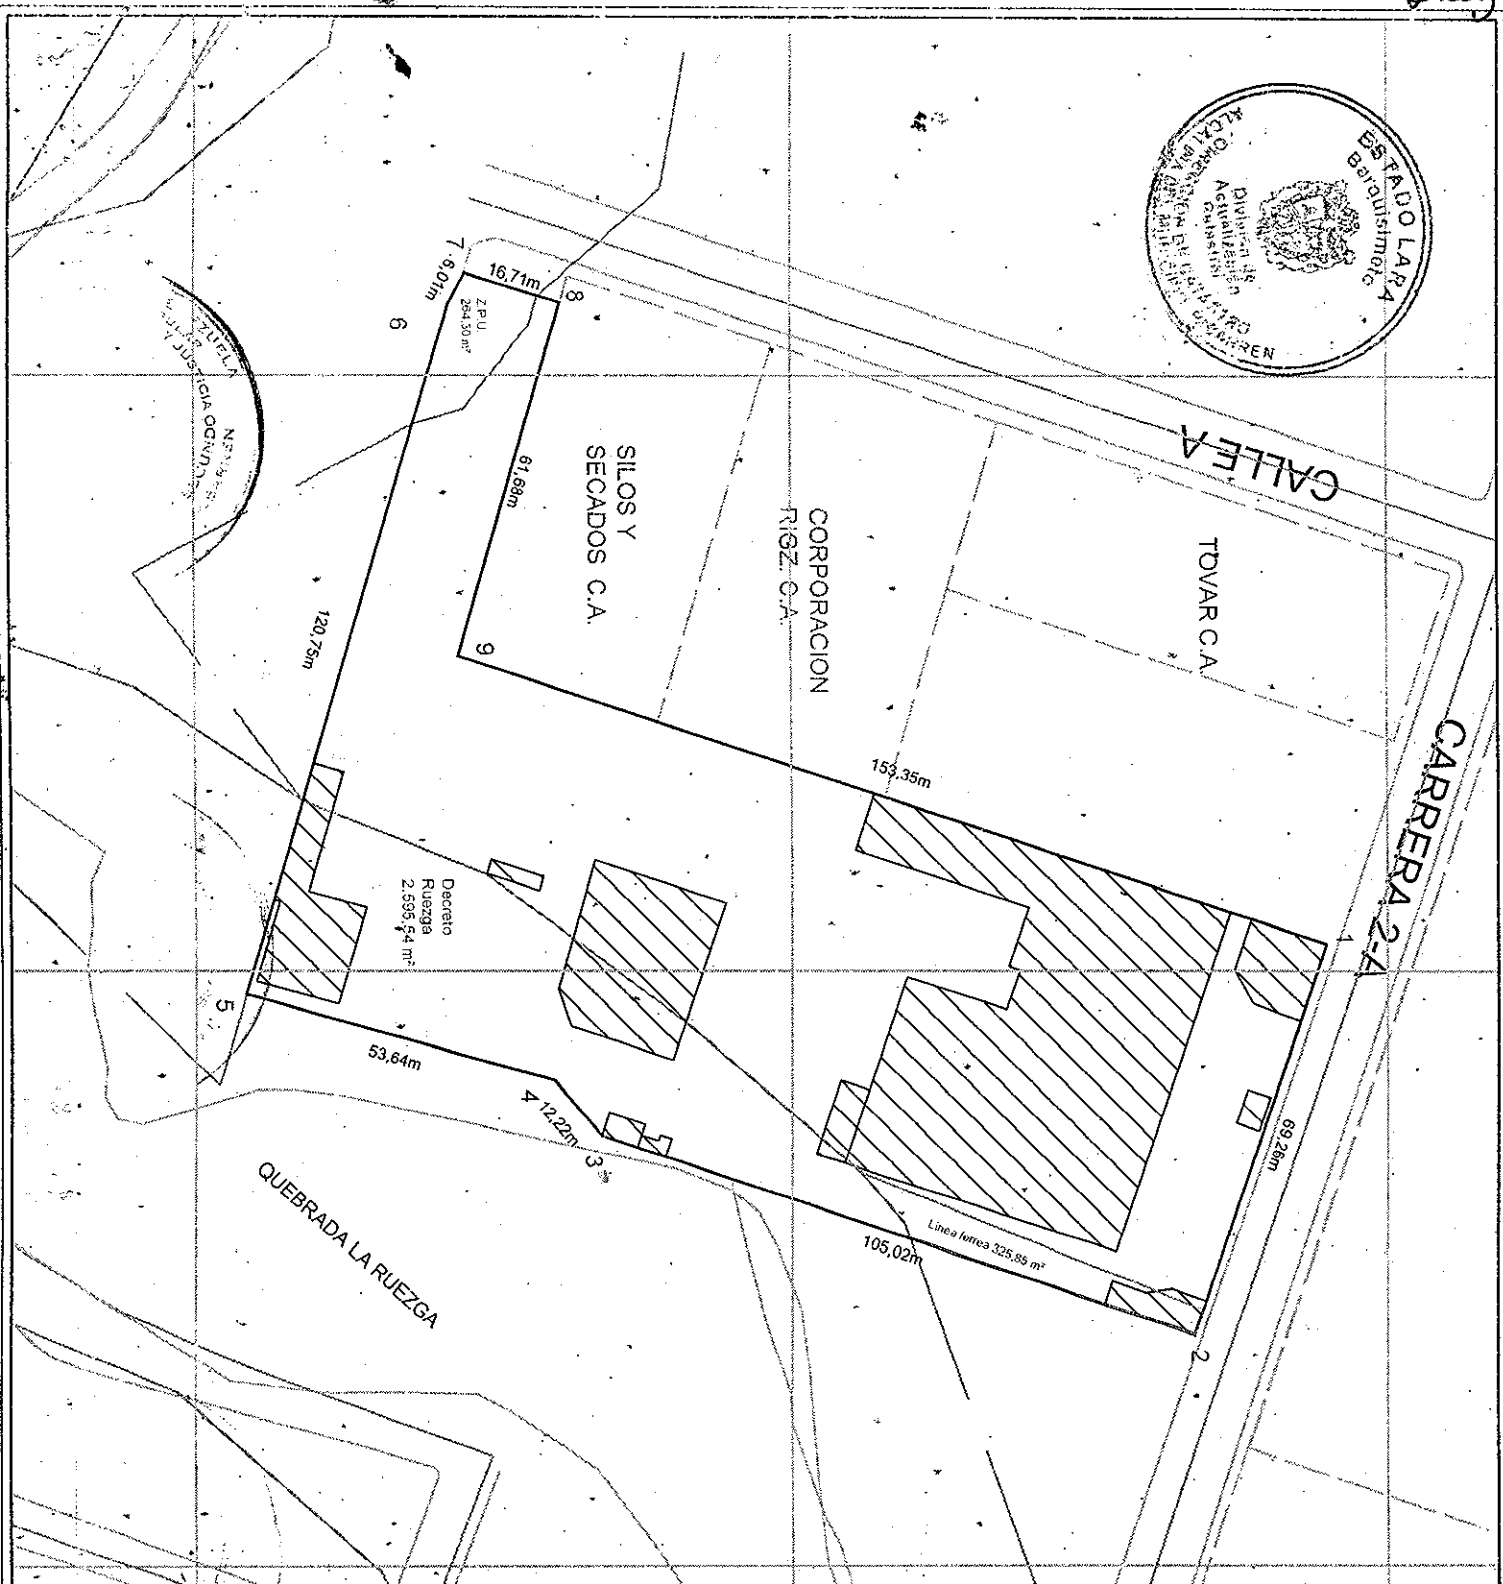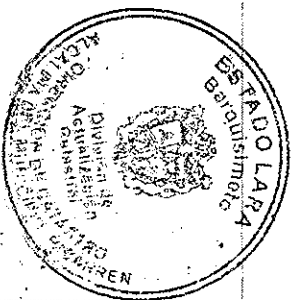


CODIGO CATASTRAL  
13-03-04-U01-017-009-013-000

| PTO | ESTE        | NORTE        |
|-----|-------------|--------------|
| 1   | 458228.0900 | 1113528.9300 |
| 2   | 458293.7170 | 1113506.7789 |
| 3   | 458260.2100 | 1113407.2500 |
| 4   | 458250.9400 | 1113399.2900 |
| 5   | 458236.4600 | 1113347.6400 |
| 6   | 458120.6600 | 1113381.8700 |
| 7   | 458115.3300 | 1113384.6500 |
| 8   | 458120.2900 | 1113400.6100 |
| 9   | 458179.5400 | 1113383.4700 |
| 1   | 458228.0900 | 1113528.9300 |

Observaciones y Antecedentes:

- 1) Se dejan a salvo derechos de terceros y del Municipio sobre la propiedad del terreno.
- 2) Sujeta a las afectaciones que esta pudiese tener en cumplimiento de la función social que ejerce el Municipio, en materia de urbanismo.
- 3) Existe una diferencia en mas de 3,411,58 m² entre el área según documento protocolizado y área del plano de mensura, ya que dicho documento presenta un error en cuanto a medidas (líderes), siendo lo correcto la cabida que el Municipio vende. Se le exhorta realizar conexión de la misma.
- 4) Igualmente, dicho excedente (Ejido), presenta una zonificación por: Zona de Protección Urbana (Z.P.U.), Línea Ferrea y Parque Recreacional La Ruezga según decreto N° 1650 de fecha 05 de Junio del año 1,991 Gaceta Oficial 4409 extraordinaria del 04 de Abril de 1992, según zonificación emitida por el Área Física adscrita a esta Dirección de fecha 26/02/2013.
- 5) Área según documento: 9,157,30 m² por la cual se otorga la presente Cédula Catastral. Área según plano de mensura: 12,568,88 m². Área ocupada fuera del documento (Ejido): 3,411,58 m².
- 6) A solicitud de parte interesada las parcelas 017-009-003-000 (ant. 223-002-009-000), 017-009-004-000 (ant. 223-002-010-000) y 017-009-009-000 (ant. 223-002-002-000) se integran dicho origen a la P.C. 017-009-013-000 (ant. 223-002-003-000).
- 7) Esta Solicitud de integración, fue realizada con antelación a la emisión del reglamento de integración y división de parcelas.
- 8) el artículo N° 67 de la Ley Orgánica de Ordenación Urbanística establece: "las parcelas integradas, serán consideradas como una unidad a los efectos urbanísticos y en ningún caso, podrán subdividirse nuevamente a los fines de su utilización."

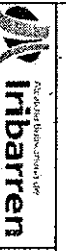

República Bolivariana de Venezuela  
Estado Lara  
Alcaldía del Municipio Inbarren  
Dirección de Catastro

PLANO DE MENSURA

BALANCE DE SUPERFICIE

ÁREA SEGÚN PLANO DE MENSURA:  
12,568,88 m²

ÁREA SEGÚN  
DOCUMENTO PROTOCOLIZADO:  
9,157,30 m²

DIFFERENCIA EN MAS  
3,411,58 m²

Solicitante:  
SILOS Y SECADOS, C.A. SISECA

Ubicación:  
ZONA INDUSTRIAL LA CARRERA 2A ENTRE CALLE  
1A QUEBRADA LA RUEZGA PARROQUIA JUAN  
DE VILLEGAS.

Objeto: Dto. 1300 Soplin Leonzo Montenegro.

Firma: *[Firma]*

N° Mapa: 6346-III-SO

Escala: 1 : 1.250 Total Hojas: 1

Número de Cédula: 192-2017

Firma del Emisor:


Firma de Dirección:



Por: *[Firma]*  
Ing. C. G. Contreras  
Alcalde del Municipio de Barquisimeto

Resolución: P.C. 017-009-013-000 del 20-09-17  
Barquisimeto, 19 de Septiembre de 2018

PROCESO DE UBICACIÓN

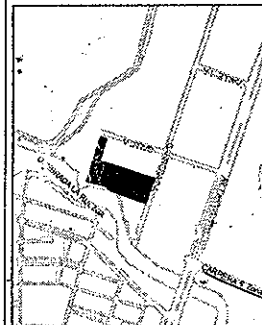

## CÉDULA CATASTRAL

Fecha: 28-02-2018  
Solicitud Nro: 192-2017

Código Verificación: 5a96f1159fe66

| PROPIETARIOS DEL INMUEBLE                            |   | CÉDULA / RIF           |               | CÓDIGO CATASTRAL     |                                                    |
|------------------------------------------------------|---|------------------------|---------------|----------------------|----------------------------------------------------|
| SILOS Y SECADO, C.A. (SISECA)                        |   | J085172874             |               | ANTERIOR             | 13-03-05-U01-223-0002-015-000                      |
|                                                      |   |                        |               | ACTUAL               | 13-03-04-U01-017-0009-013-000                      |
| DIRECCIÓN                                            | CARRERA 2A ENTRE CALLE 1A QUEBRADA LA RUEZGA                                                                                          |                        |               |                      |                                                    |
| SECTOR / URB                                         | ZONA INDUSTRIAL III   | NÚMERO                 | S/Nº          | PARROQUIA            | Juan de Villegas                                   |
| BALANCE DE SUPERFICIE                                |   |                        |               |                      |                                                    |
| Área Original                                        |   | Área Actual            |               | Diferencia           |                                                    |
| 9.157,30 (m²)                                        |   | 12.568,88 (m²)         |               | 3.411,58 (m²)        |                                                    |
| DATOS DE LOS DOCUMENTOS DE PROPIEDAD                 |   |                        |               |                      |                                                    |
| Número                                               | Asto.Reg./ Tomo   | Matrícula / Prot.      | Folio         | Fecha                | Entidad Pública Legal                              |
| 2017.667                                             | 1   | 363.11.2.7.5268        | Real Año 2017 | 20-10-2017           | Registro Público del Segundo Circuito de Iribarren |
| LINDEROS ORIGINALES S/Nº                             |   |                        |               |                      |                                                    |
| NORTE                                                | En dos líneas de: (61,68 Mts) y (69,91 Mts) con Carrera 2-A.                                                                          |                        |               |                      |                                                    |
| SUR                                                  | En dos líneas de: (6,01 mts) y (120,75 Mts), con terreno desocupado.                                                                  |                        |               |                      |                                                    |
| ESTE                                                 | En tres líneas de: (104,63 Mts), con Proyecto de canalización del parque la Ruezga y (2,22 Mts), (53,64 Mts), con Quebrada la Ruezga. |                        |               |                      |                                                    |
| OESTE                                                | En dos líneas de: (153,35 Mts) y (16,71 Mts), con la Calle 1A.                                                                        |                        |               |                      |                                                    |
| LINDEROS ACTUALES                                    |   |                        |               |                      |                                                    |
| NORTE                                                | Con parcela que es o fue de Silos y Secados, C.A. y Carrera 2A de la referida Zona Industrial, que es su frente.                      |                        |               |                      |                                                    |
| SUR                                                  | Con Quebrada la Ruezga.   |                        |               |                      |                                                    |
| ESTE                                                 | Con Quebrada la Ruezga.   |                        |               |                      |                                                    |
| OESTE                                                | Con parcela que es o fue de Silos y Secados, C.A.; Corporación Rigz, C.A. y Tovar, C.A.                                               |                        |               |                      |                                                    |
| VALOR TERRENO                                        |   | VALOR CONSTRUCCIÓN     |               | TOTAL VALOR INMUEBLE | Nº MAPA CATASTRAL                                  |
| 4.293.857,97 Bs                                      |   | 55.339.876,80 Bs       |               | 59.633.734,77 Bs     | 6346-III-SO                                        |
| INFORMACIÓN SOLO PARA FINES FISCALES                 |   |                        |               |                      |                                                    |
| RÉGIMEN DE PROPIEDAD                                 |   | ÁREA ORIGINAL TERRENO  |               | TOTAL ÁREA ORIGINAL  | ÁREA ACTUAL                                        |
| Privado individual                                   |   | 9.157,30 (m²)          |               | 9.157,30 (m²)        | 12.568,88 (m²)                                     |
| BASE IMPONIBLE PARA DETERMINAR IMPUESTO INMOBILIARIO |   |                        |               |                      |                                                    |
| ÁREA FISCAL DE TERRENO                               |   | TIPOLOGÍA CONSTRUCCIÓN |               | USO                  | ÁREA CONSTRUCCIÓN                                  |
| 9.157,30 (m²)                                        |   | Galpon Industrial      |               | Industrial           | 4.112,96 (m²)                                      |

**OBSERVACIONES:**

- 1) Se dejan a salvo derechos de terceros y del Municipio sobre la propiedad del terreno.
- 2) Sujeta a las afectaciones que esta pudiese tener en cumplimiento de la función social que ejecuta el Municipio, en materia de urbanismo.
- 3) Existe una diferencia en más de 3.411,58 m<sup>2</sup> entre el Área según documento protocolizado y Área del plano de mensura, ya que dicho documento presenta un error en cuanto a medidas (linderos), siendo lo correcto la cabida que el Municipio vende. Se le exhorta realizar corrección de la misma.
- 4) Igualmente dicho excedente (Ejido) presenta una Zonificación por: Zona de Protección Urbana (Z.P.U.), Línea Ferrea y Parque Recreacional La Ruezga según Decreto N° 1.650 de fecha 05 de Junio del Año 1.991 Gaceta Oficial 4409 Extraordinaria del 04 de Abril del Año 1992, según Zonificación emitida por el Área Física adscrita a esta Dirección en fecha 26/02/2018.
- 5) Área según documento: 9.157,30 m<sup>2</sup> por la cual se otorga la presente Cédula Catastral; Área según Plano de Mensura: 12.568,88 m<sup>2</sup>. Área ocupada fuera del documento (Ejido): 3.411,58 m<sup>2</sup>.
- 6) A solicitud de parte interesa las parcelas 017-0009-003-000 (Ant.223-0002-009-000); 017-0009-004-000 (Ant.223-0002-010-000) y 017-0009-005-000 (Ant.223-0002-002-000) se integran dando origen a la Pc. 017-0009-013-000 (Ant. 223-0002-015-000).
- 7) Esta solicitud de integración, fue realizada con antelación a la emisión del Reglamento de Integración y División de Parcelas.
- 8) El Artículo N° 67 de la Ley Orgánica de Ordenación Urbanística establece: "Las parcelas integradas, serán consideradas como una unidad a los efectos Urbanísticos y en ningún caso, podrán subdividirse nuevamente a los fines de su utilización."



Christian E. Mendoza C  
Director de Catastro

Resolución N° RRH/AL 211-2017 del 20-09-2017  
DIRECCIÓN DE



| Retirado por | Cédula de Identidad | Fecha    | Firma   | Revisado por |
|--------------|---------------------|----------|---------|--------------|
| JOSE VIDAL   | 7.306.893           | 11/05/18 | [Firma] | [Firma]      |

Elaborado por : Francis D. Colmenarez B.